DEDICATION

KNOW ALL MEN BY THESE PRESENTS, THAT WE, C.H. OVERMAN, INDIVIDUALLY, AND AS TRUSTEE, AND ARNETTE S. OVERMAN, HIS WIFE, OWNERS OF THE LAND HEREON SUBDIVIDED HEREBY DEDICATE TO THE PUBLIC ALL OF THE STREETS AND ROADS AS DESIGNATED ON SAID PLAT.

SIGNED, SEALED AND DELIVERED IN THE PRESENCE OF:

C.H. Overman Jr.

H.P. Edwards

C.H. Overman (Seal)
INDIVIDUALLY, AND AS TRUSTEE

Arnette S. Overman (Seal)


STATE OF FLORIDA
COUNTY OF LEON

BEFORE THE SUBSCRIBER PERSONALLY APPEARED C.H. OVERMAN, TRUSTEE, AND ARNETTE S. OVERMAN, HIS WIFE KNOWN TO ME TO BE THE INDIVIDUALS DESCRIBED IN AND WHO EXECUTED THE FOREGOING INSTRUMENT, AND ACKNOWLEDGED THAT THEY EXECUTED THE SAME FOR THE USES AND PURPOSES THEREIN SET FORTH, AND THE SAID C.H. OVERMAN ACKNOWLEDGED THAT HE EXECUTED THE SAME AS TRUSTEE.

GIVEN UNDER MY HAND AND OFFICIAL SEAL THIS 15TH DAY OF MARCH, 1947

Lottie Lee Campbell
NOTARY PUBLIC STATE OF FLORIDA AT LARGE

MY COMMISSION EXPIRES Jan. 23, 1950

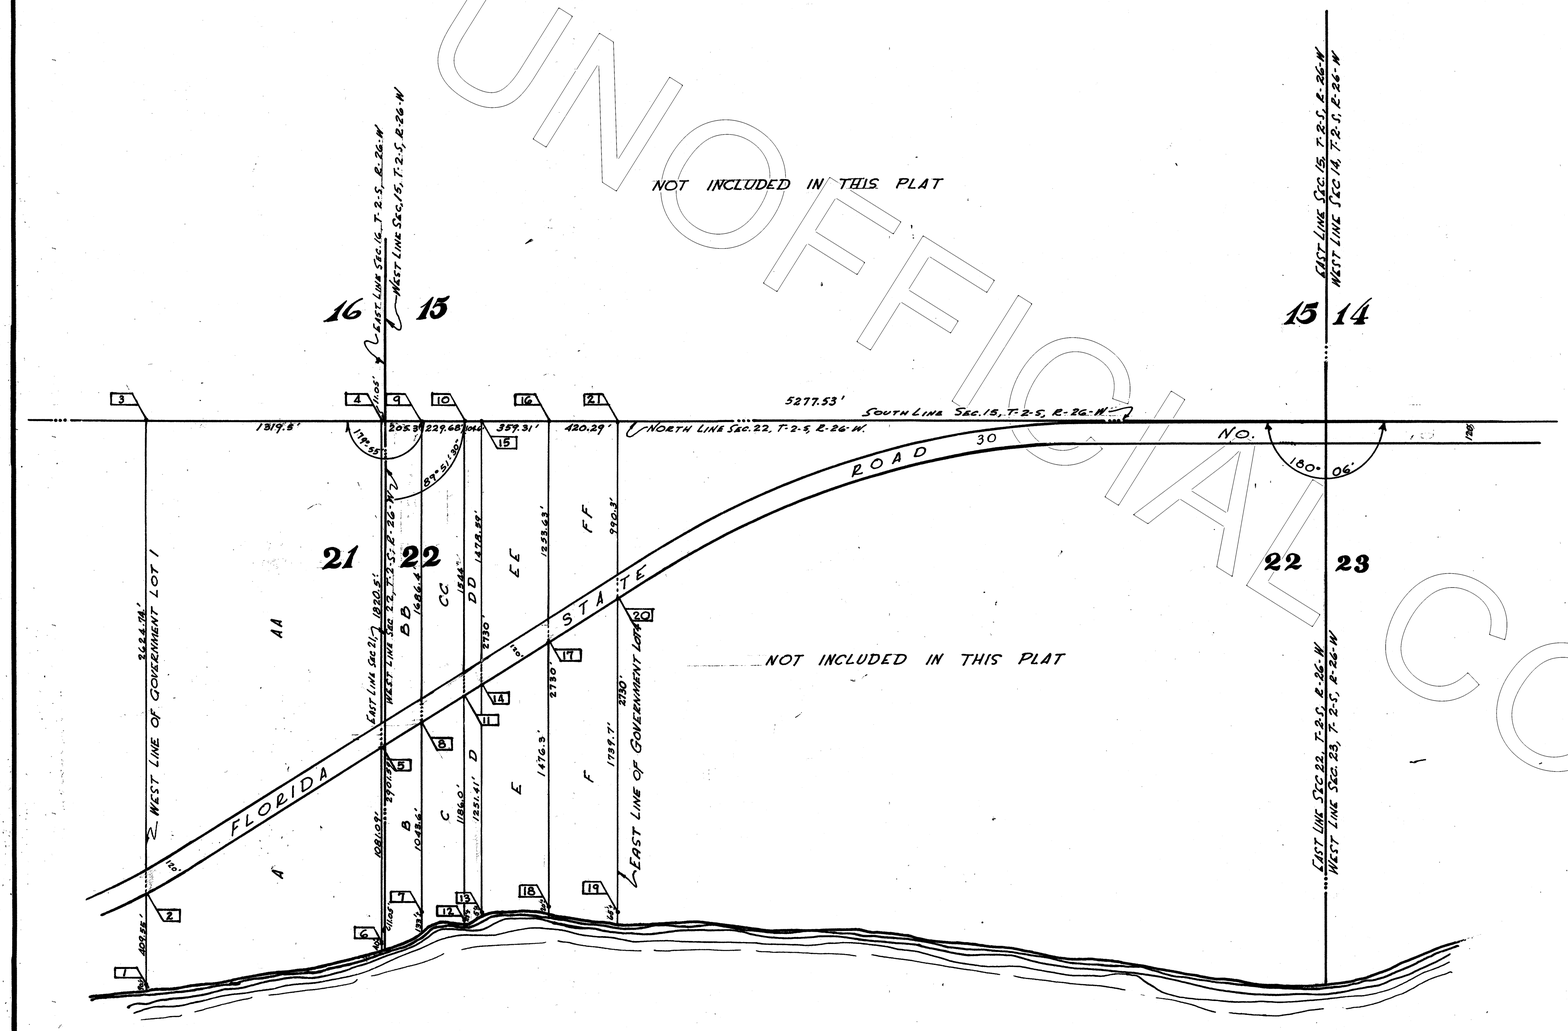

COUNTY CLERK'S CERTIFICATE

I, C.E. LOCKLIN, CLERK OF THE CIRCUIT COURT, OF SANTA ROSA COUNTY, FLORIDA, HEREBY CERTIFY THAT THIS PLAT COMPLIES WITH ALL THE REQUIREMENTS OF THE PLAT ACT (CHAPTER 10275 OF THE 1925 ACTS OF THE LEGISLATURE OF FLORIDA) AND THE SAME WAS FILED FOR THE RECORD ON THE 8TH DAY OF APRIL 1947 AND FILED AT PAGE 70 OF PLAT BOOK "A" OF SAID COUNTY

C.E. Locklin
CLERK OF CIRCUIT COURT
SANTA ROSA COUNTY, FLORIDA

crescent shores

SANTA ROSA COUNTY, FLORIDA
SECTIONS 13, 14, 15, 16, 21, 22, 23, AND 24
TOWNSHIP - 2 - SOUTH, RANGE - 26 - WEST.
BY C. H. OVERMAN, C.E.
SCALE 1" - 400' DECEMBER, 1946
PENSACOLA, FLORIDA

CERTIFICATE OF APPROVAL OF COUNTY COMMISSIONERS

I, C.E. LOCKLIN, COUNTY CLERK OF SANTA ROSA, COUNTY, FLORIDA, HEREBY CERTIFY THAT THE WITHIN PLAT, BEING PRESENTED TO THE BOARD OF COUNTY COMMISSIONERS OF SAID COUNTY AT THEIR MEETING HELD ON THE 8TH DAY OF APRIL, 1947 WAS APPROVED FOR FILING BY THE SAID BOARD AND I, AS CLERK OF SAID BOARD, WAS INSTRUCTED TO SO CERTIFY HEREON.

C.E. Locklin
COUNTY CLERK SANTA ROSA COUNTY FLORIDA

SURVEYOR'S CERTIFICATE

THE UNDERSIGNED HEREBY CERTIFIES THAT THIS PLAT IS A CORRECT REPRESENTATION OF THE LAND HEREON DESCRIBED; THAT THE LAND HAS BEEN SUBDIVIDED AND STAKED AS INDICATED; THAT PERMANENT REFERENCE MONUMENTS (INDICATED P.R.M.) HAVE BEEN PLACED AS REQUIRED BY PLAT ACT (CHAPTER 10275); THAT THE SIGN (') MEANS FEET OR MINUTES AND THAT THE SIGN (°) MEANS DEGREES. ☐ CARRIES NUMBER ON P.R.M. THIS PLAT CONSISTS OF 2 SHEETS.

C.H. Overman Jr.
REGISTERED FLORIDA LAND SURVEYOR NO 475.

SHEET 1 OF 2

UNOFFICIAL COPY

UNOFFICIAL COPY

NOT INCLUDED IN THIS PLAT

OLD FENCE

OLD FENCE
EGLIN FIELD MARKER No. 3

EGLIN FIELD MARKER No. 2

EAST LINE SEC. 15, T-2-S, R-26-W.
WEST LINE SEC. 14, T-2-S, R-26-W.

EAST LINE SEC. 22, T-2-S, R-26-W.
WEST LINE SEC. 23, T-2-S, R-26-W.

EAST LINE SEC. 13, T-2-S, R-26-W.

WEST LINE OF EAST ½

EAST LINE OF W½ OF SW¼

WEST LINE GOVERNMENT LOT 1

NORTH LINE SEC. 23, T-2-S, R-26-W

SOUTH LINE SEC. 13, T-2-S, R-26-W

COUNTY LINE

FLA. ROAD NO. 30

SANTA ROSA SOUND

NOT INCLUDED IN THIS PLAT

CRESCENT SHORES
SHEET 2 of 2